
Маркировочный план фрагмента в осях 6-8/Г-К 2 этажа (1 : 75)

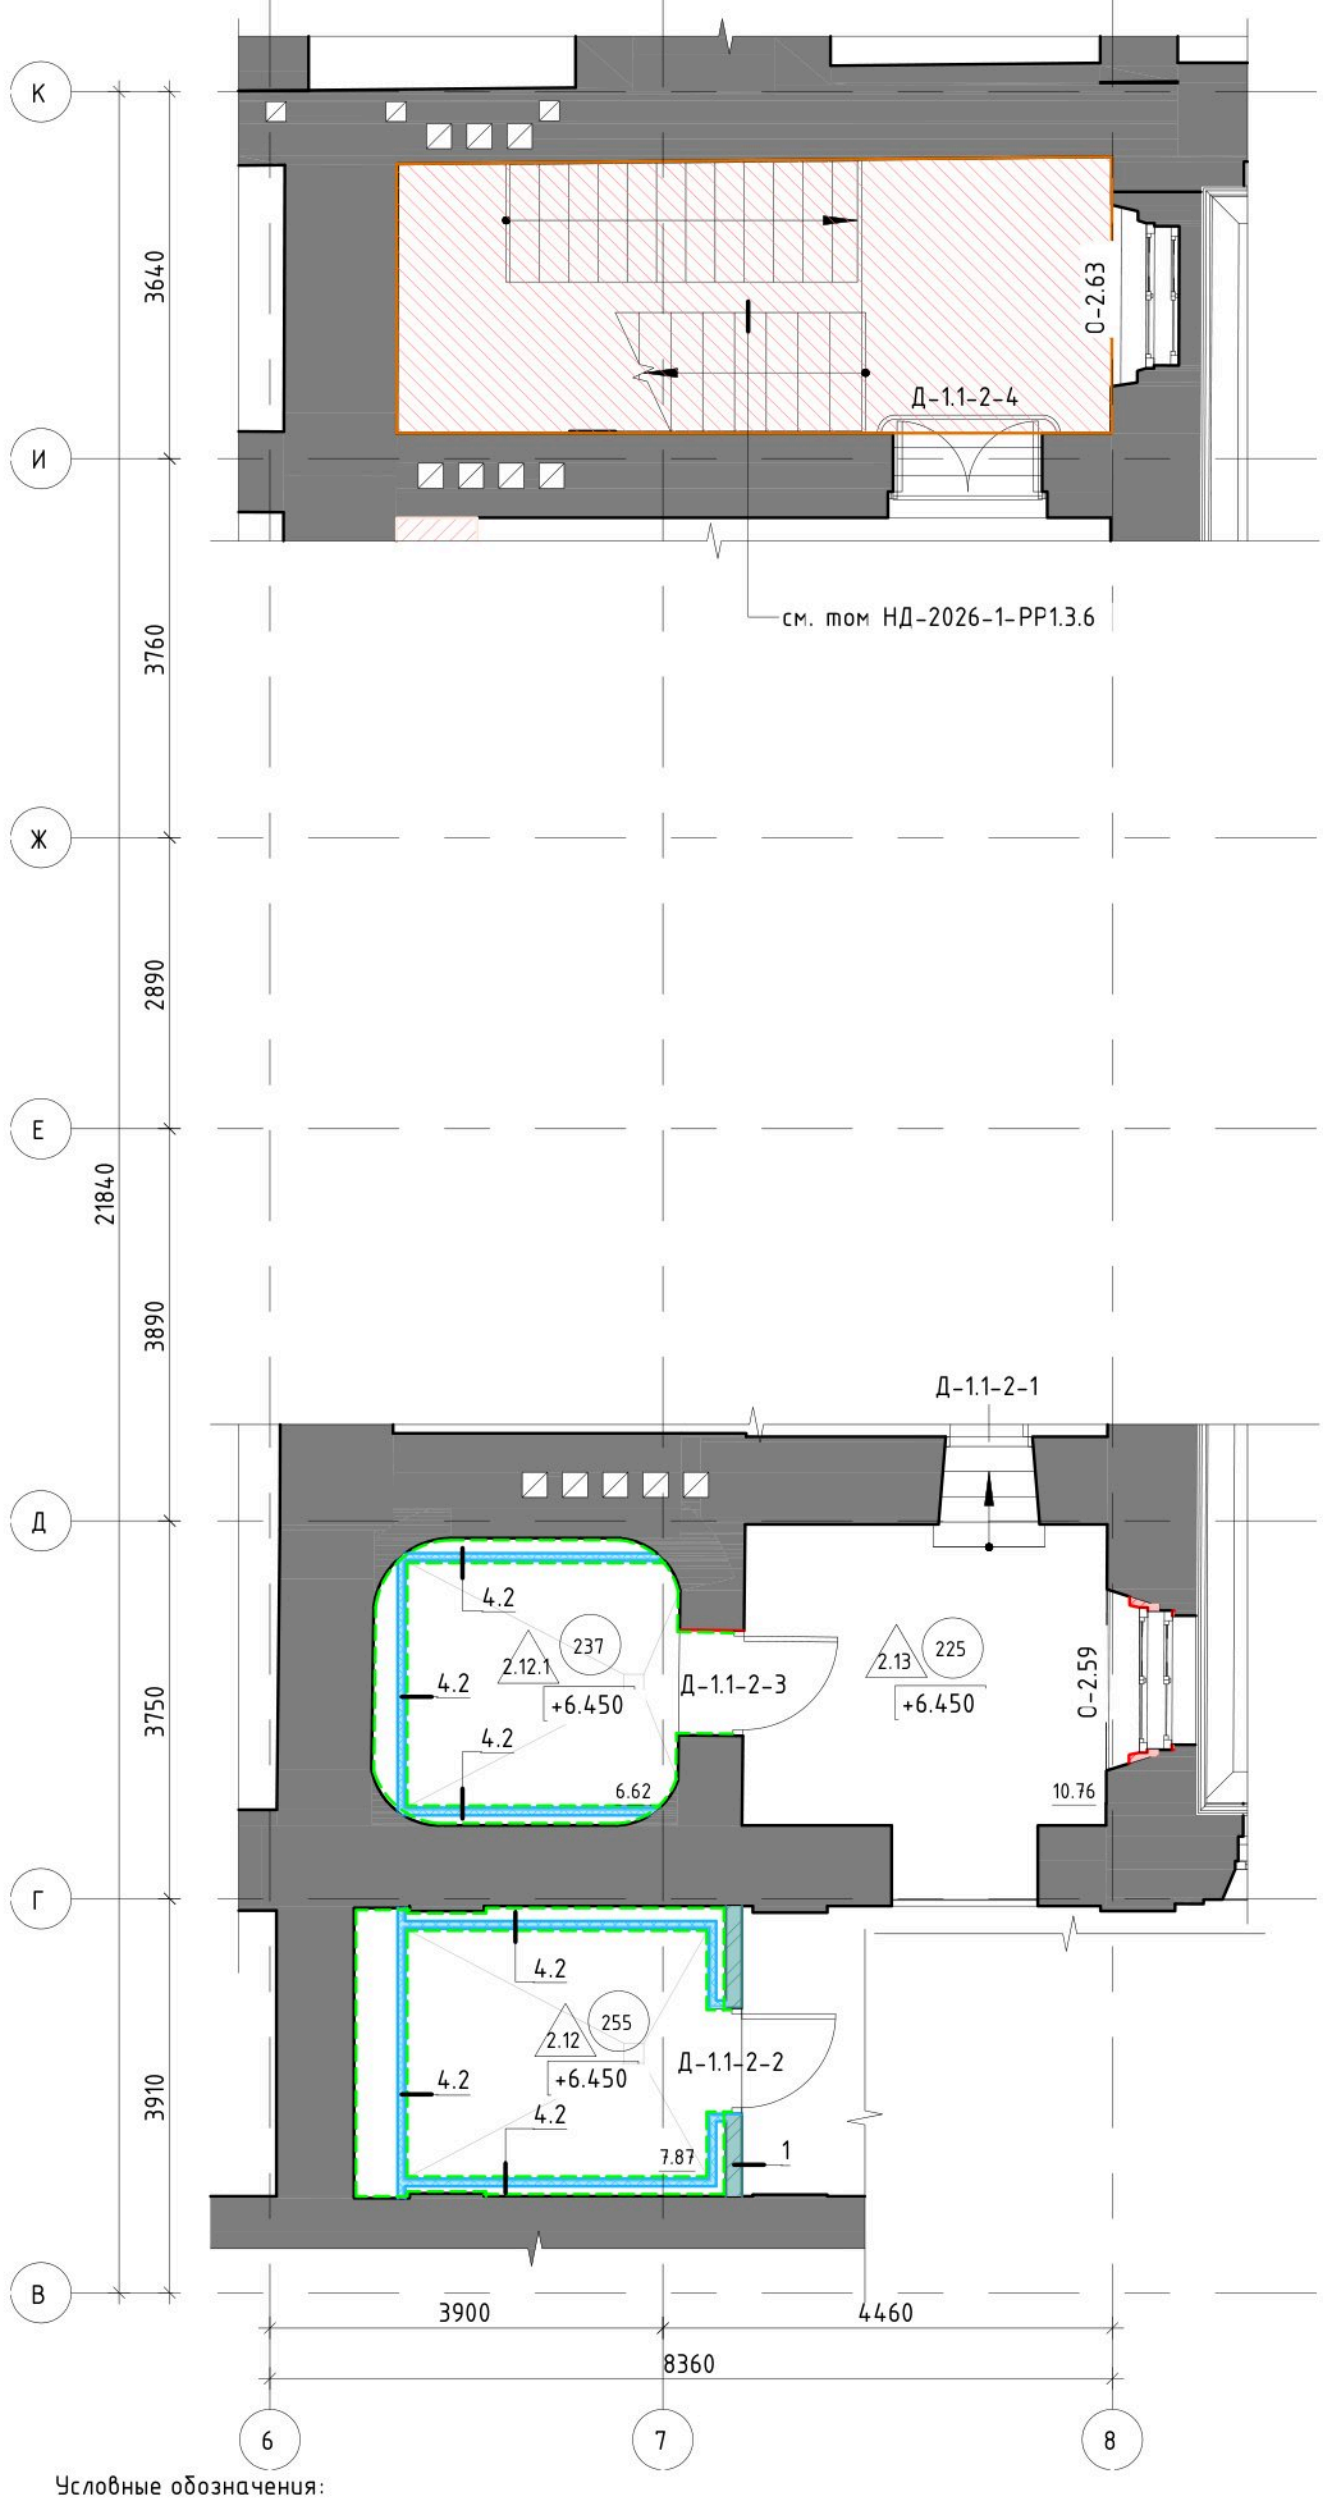

Условные обозначения:

- 1 – Ось координации
- +0,000 – Отметка уровня
- – Реставрируемые помещения
- – Сохраняемые конструкции
- – Пробиваемый проем
- – Закладываемый проем
- – Рядовая перегородка с обшивкой ГКЛ-листами
- – Влагостойкая перегородка с обшивкой КНАУФ-листами АКВАПАНЕЛЬ
- – Огнестойкая перегородка обшивкой КНАУФ-листами ФАЙЕРБОРД
- – Перегородка из бетонного камня
- 1.1 – Марка пола
- – См
- – Сб
- – Ак
- Д-1.1-1-1П – Ма
- О-1.1 – Ма

Спецификация элементов заполнения две

Марка дверного заполнения	Обозначение	Наименование	Габариты проем по полотну		Кол-во			
			Высота, мм	Ширина, мм		Огн.-ст	R. дБ	
Д-1.1-2-1	ГОСТ 475-2016	ДМ 1Рл 21х9 ПрБ МдЗ	1990	780	1	-	-	Тип открывания, коли Тип дверного блока: с доводчика, петель, по прямые петли, без пор Тип ручки: нажимная электромеханический
Д-1.1-2-2	ГОСТ 475-2016	ДС 1Рп 21х10.5 Пр МдЗ	1990	930	1	-	-	Тип открывания, коли Тип дверного блока: с доводчика, петель, по прямые петли, выпада ограничитель; Тип отсутствует
Д-1.1-2-3	ГОСТ 475-2016	ДС 1Рп 21х10.5 Пр МдЗ	1990	930	1	-	-	Тип открывания, коли Тип дверного блока: с доводчика, петель, по прямые петли, выпада ограничитель; Тип отсутствует
Д-1.1-2-4	ГОСТ 475-2016	ДМ 2Р 21.8х15.8 ПрБ МдЗ	2090	1400	1	-	-	Тип открывания, коли дверного блока: откр доводчика, петель, по фиксатором на обе ст доводчик ограничите СКУД: электромехани
					4			

1. Данный лист смотреть совместно листами 6, 23-25 данного тома;
2. Общая спецификация возводимых стен и перегородок дана на листе 24 данного тома;
3. Общая спецификация экспликация устраиваемых полов дана на листе 23 данного тома;
4. Общая спецификация элементов дверных и оконных заполнений дана на листе 25 данного тома;
5. Маркировка проемов и ниш сквозная по этажу фрагмента, дана в стенах и перегородках;
6. Узлы устройства перегородок см. технологические карты, альбомы технических решений и комплектных систем производителей (см. лист 1 данного тома);
7. Уточнить раскладку балок и количество кирпичных столбиков после демонтажа напольного покрытия
8. Уточненные конструктивные схемы опирания лаг и балок представлены в томе НД-2026-1-1.1-КР
9. Реставрационные чертежи см. тома НД-2026-1-1.1-РР.АИ1-АИ3;
10. Реставрационные чертежи столярных дверных и оконных заполнений см. тома НД-2026-1-1.1-РР.ДВ, НД-2026-1-1

Согласовано

Взам. инв. №

Подп. и дата

Инв. № подл.