
Маркировочный план фрагмента 3 этажа в осях 6-8/Г-К (1 : 75)

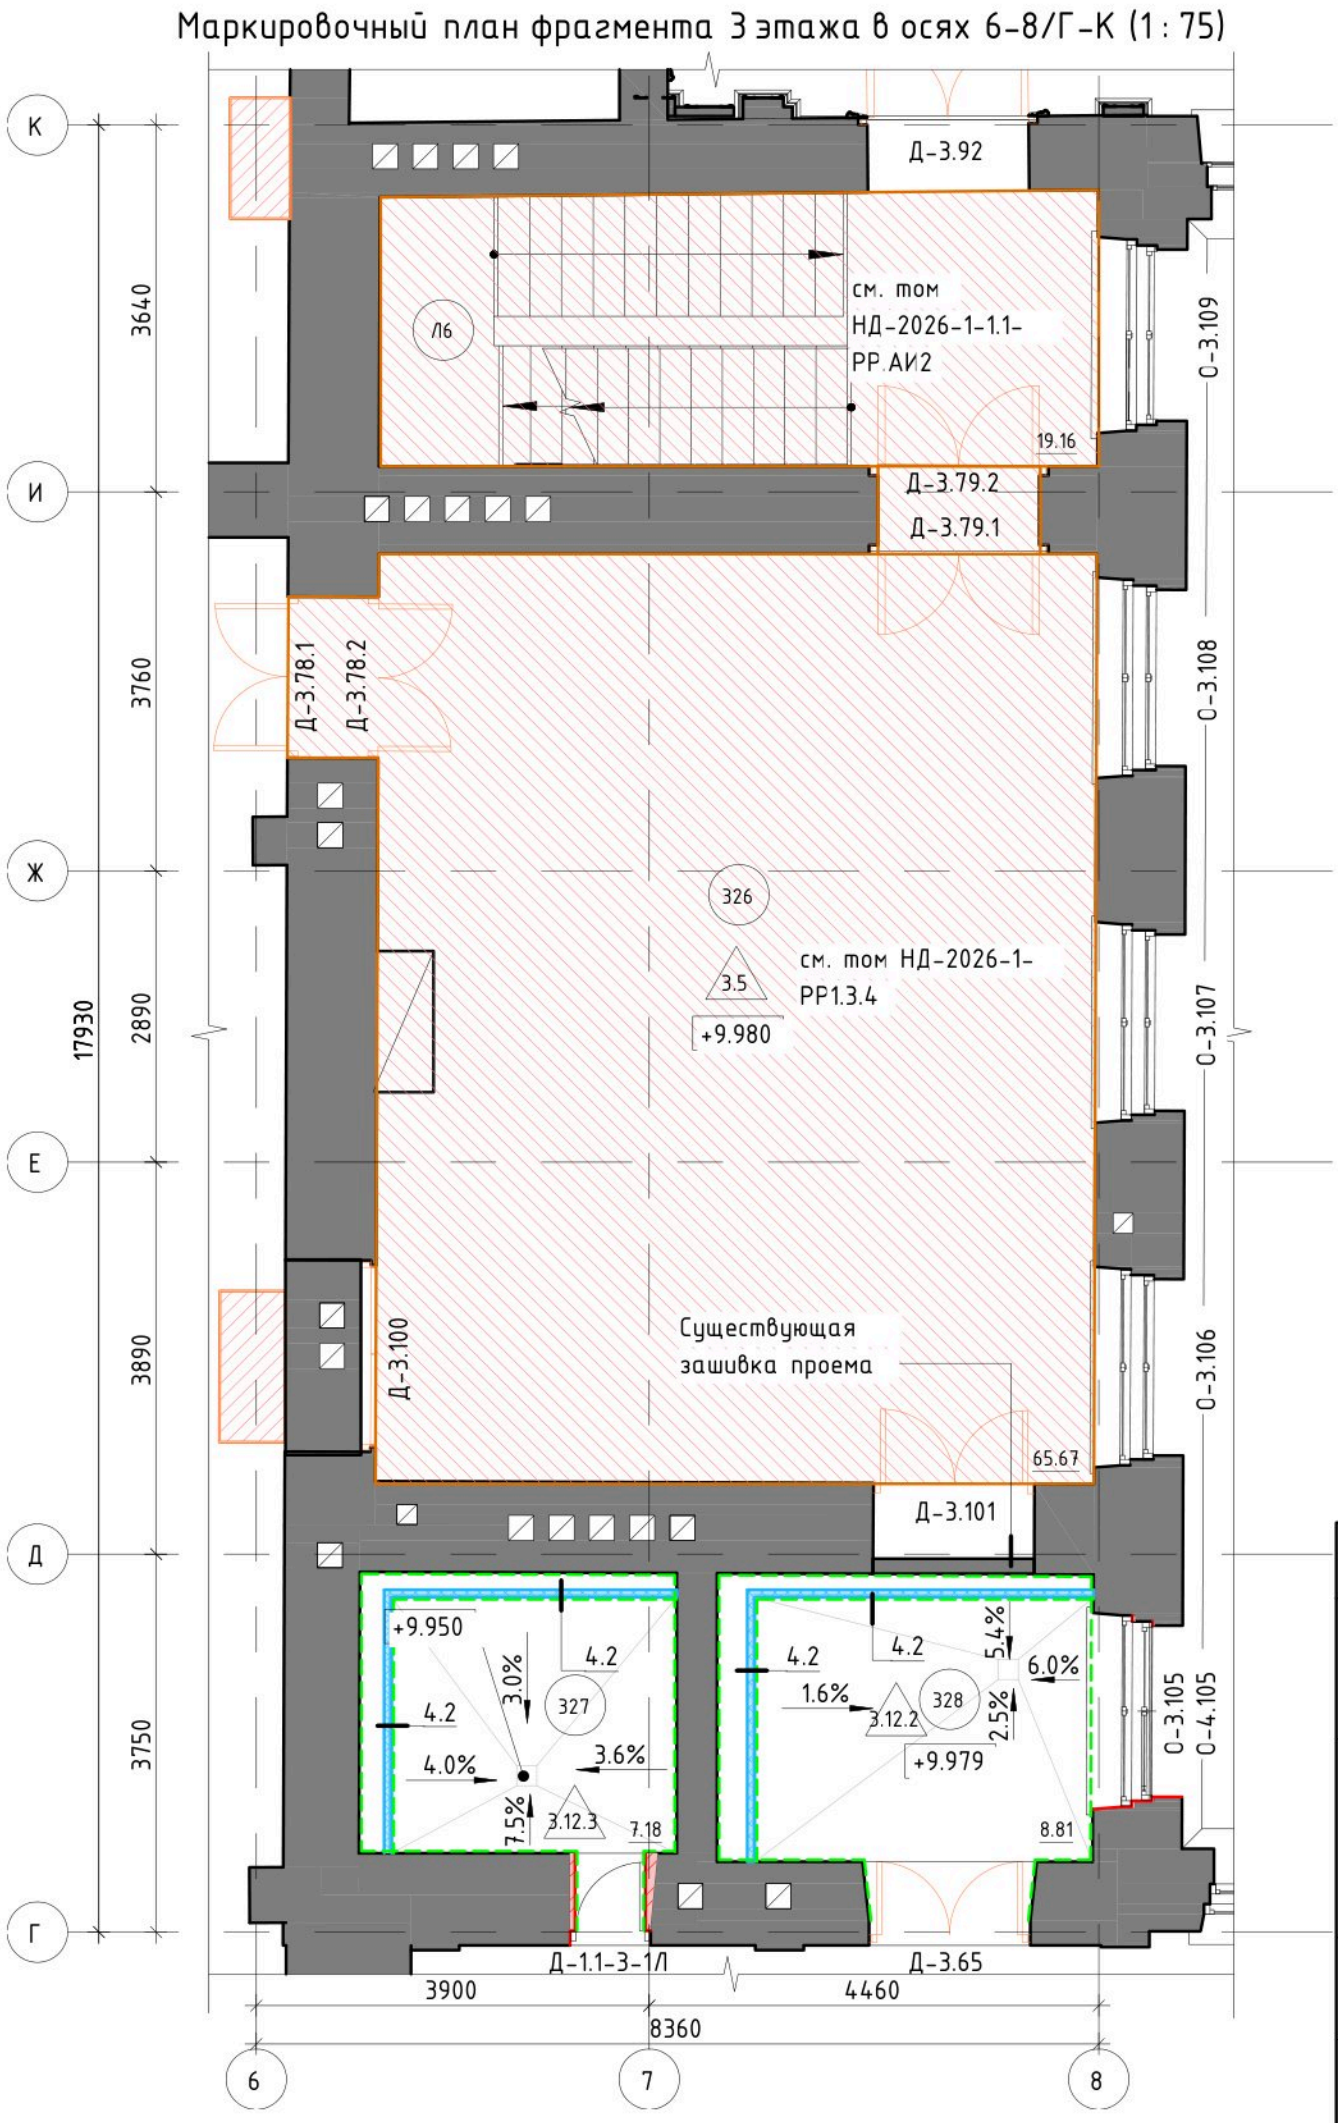

Экспликация	
Номер	
326	Холл
327	С/У
328	С/У МГН
Л6	Лестничн

Ведомость возв	
Марка	
4.2	КН ти

Марка дверного заполнения	
Д-1.1-3-1Л	Г
Д-3.65	НД
Д-3.79.1	НД
Д-3.79.2	НД
Д-3.92	НД
Д-3.100	НД
Д-3.101	НД

1. Данный лист смотреть совместно листами 7, 23-25 данного тома;
2. Общая спецификация возводимых стен и перегородок дана на листе 24 данного тома;
3. Общая спецификация экспликация устраиваемых полов дана на листе 23 данного тома;
4. Общая спецификация элементов дверных и оконных заполнений дана на листе 25 данного тома;
5. Маркировка проемов и ниш сквозная по этажу фрагмента, дана в стенах и перегородках;
6. Узлы устройства перегородок см. технологические карты, альбомы технических решений и комплектных систем производителей (см. лист 1 данного тома);
7. Уточнить раскладку балок и количество кирпичных столбиков после демонтажа напольного покрытия
8. Уточненные конструктивные схемы опирания лаг и балок представлены в томе НД-2026-1-1.1-КР
9. Реставрационные чертежи см. тома НД-2026-1-1.1-РР.АИ1-АИ3;
10. Реставрационные чертежи столярных дверных и оконных заполнений см. тома НД-2026-1-1.1-РР.ДВ, НД-2026-1-1.1-РР.ОК.

Условные обозначения:

- 1 – Ось координации
- +0,000 – Отметка уровня
- – Реставрируемые помещения
- – Сохраняемые конструкции
- – Пробиваемый проем
- – Закладываемый проем

Согласовано

Взам. инв. №

Подп. и дата

Инв. № подл.