
Маркировочный план фрагмента 5 этажа в осях 4-12/Г-С (1 : 75)

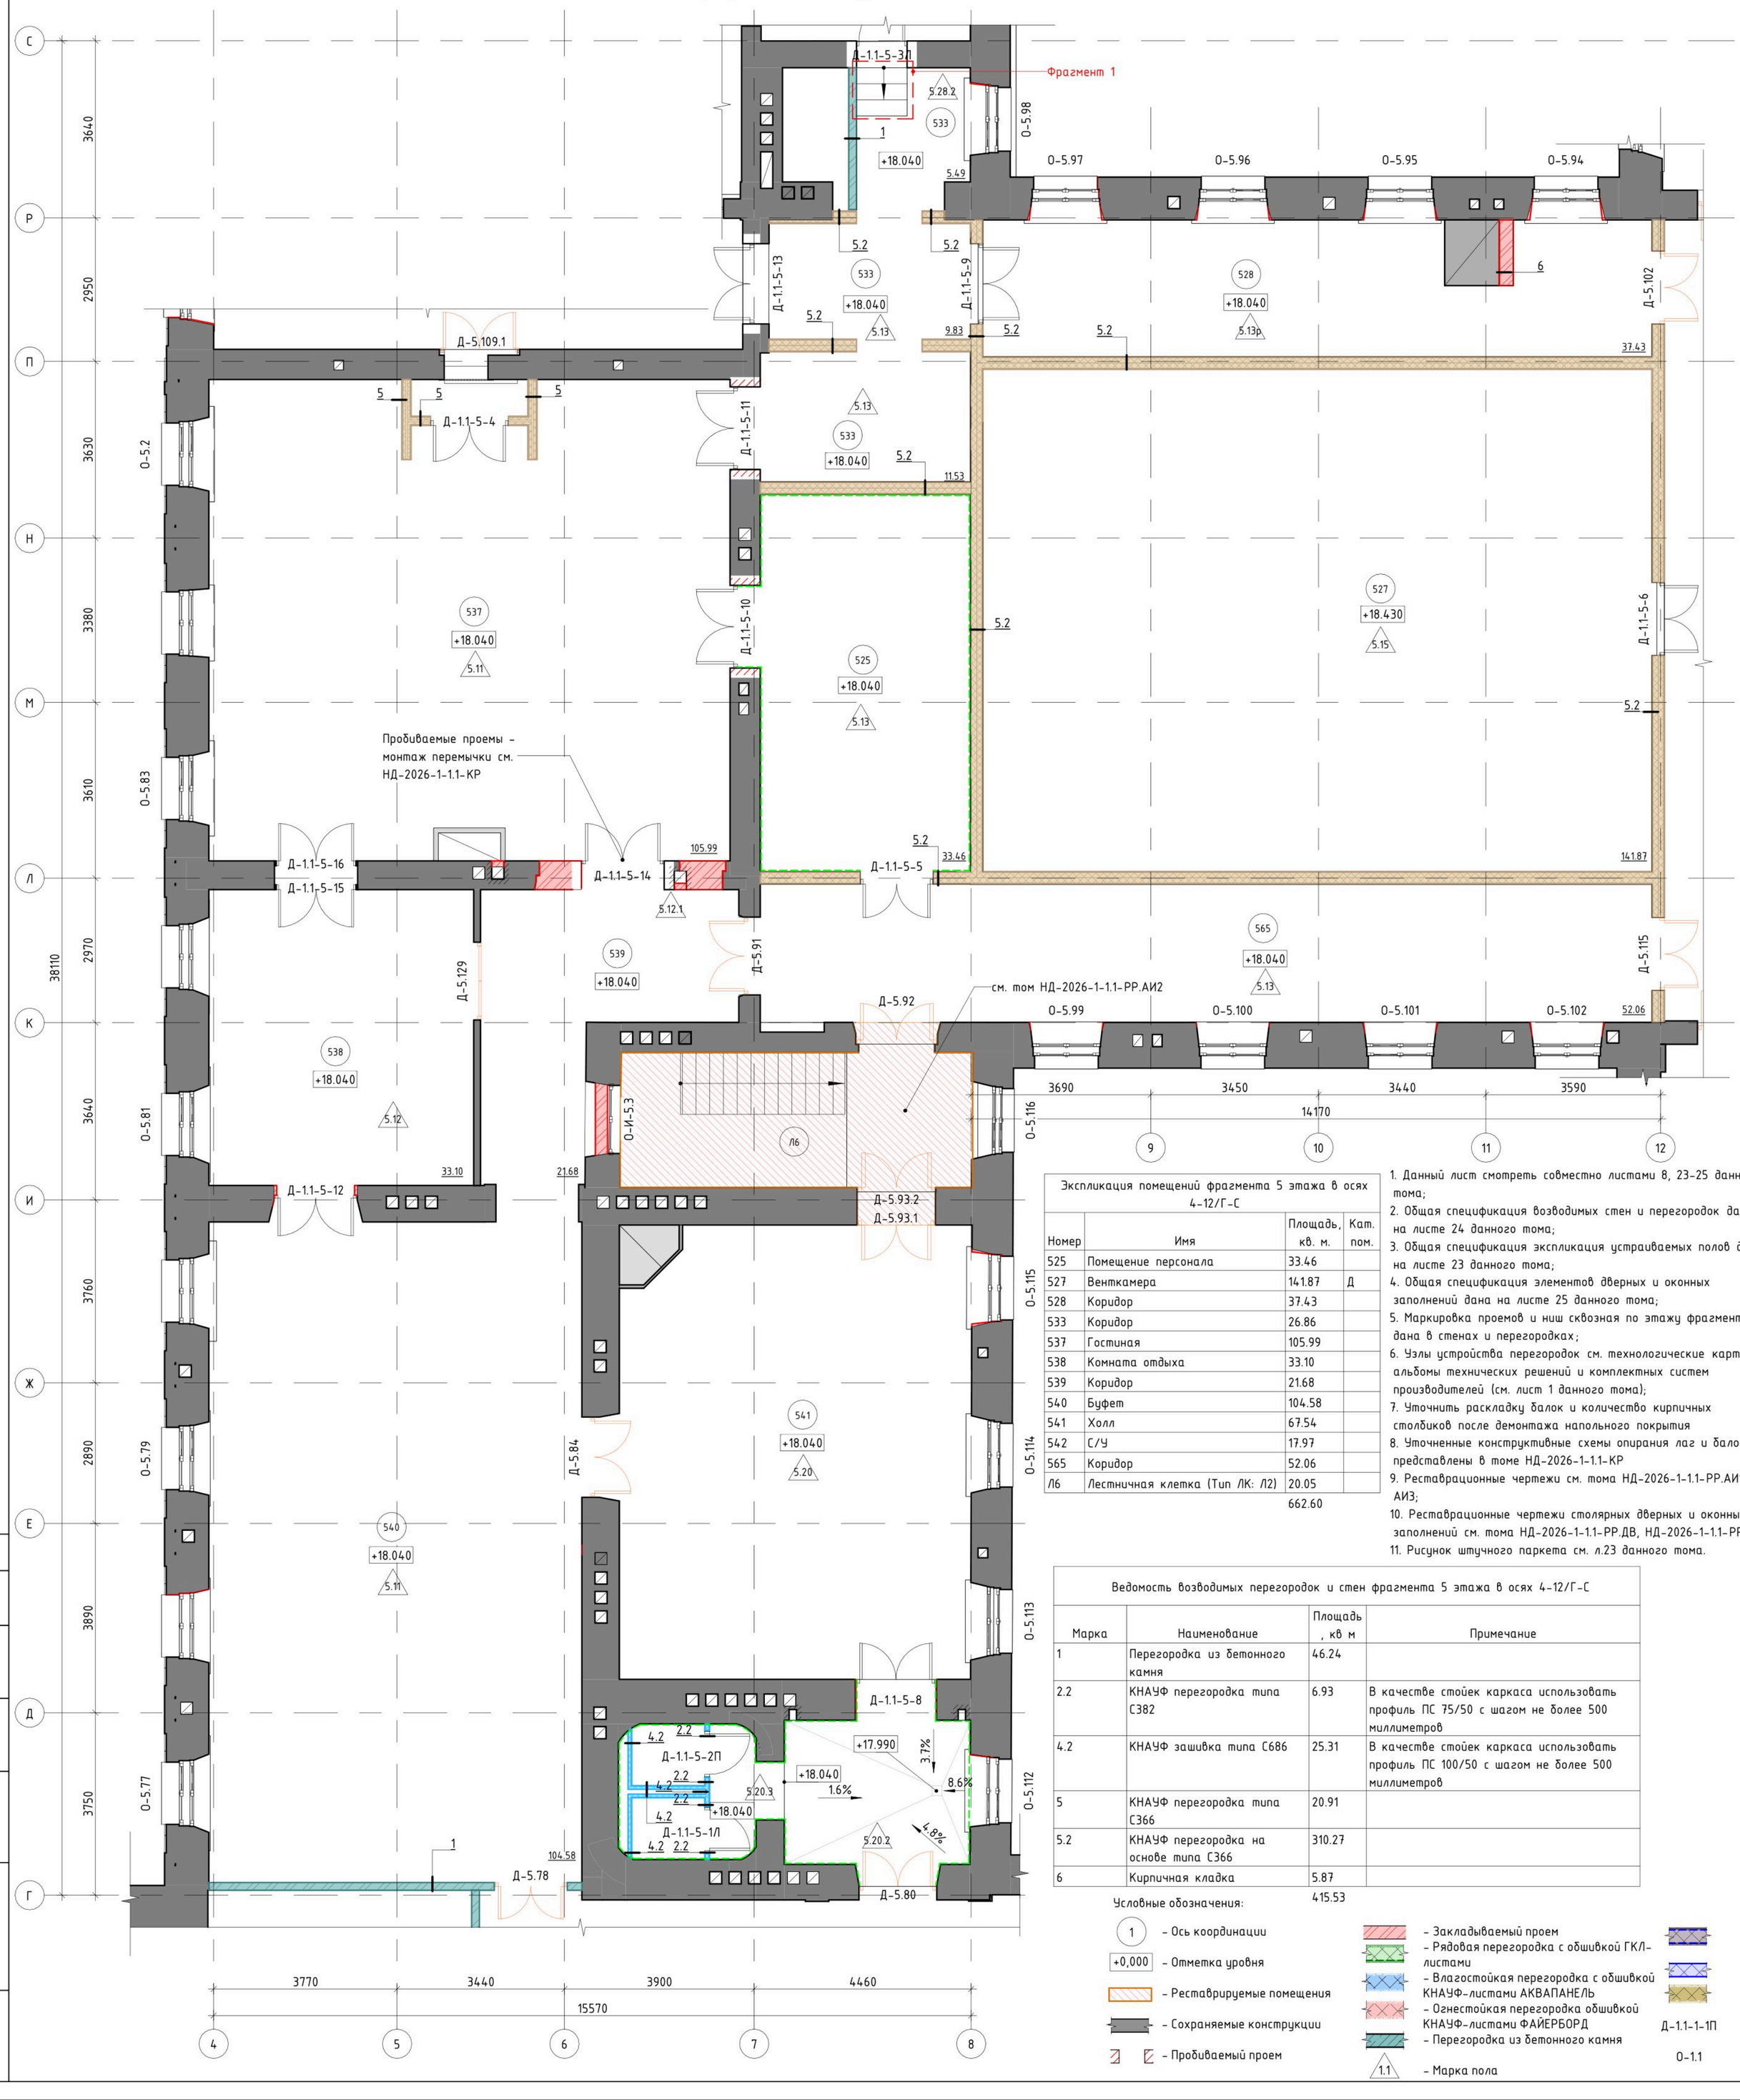

Экспликация помещений фрагмента 5 этажа в осях 4-12/Г-С			
Номер	Имя	Площадь, кв. м.	Кат. пом.
525	Помещение персонала	33.46	
527	Венткамера	141.87	Д
528	Коридор	37.43	
533	Коридор	26.86	
537	Гостиная	105.99	
538	Комната отдыха	33.10	
539	Коридор	21.68	
540	Буфет	104.58	
541	Холл	67.54	
542	С/У	17.97	
565	Коридор	52.06	
Л6	Лестничная клетка (Тип ЛК: Л2)	20.05	
		662.60	

1. Данный лист смотреть совместно листами 8, 23-25 данного тома;
2. Общая спецификация возводимых стен и перегородок дана на листе 24 данного тома;
3. Общая спецификация экспликация устраиваемых полов дана на листе 23 данного тома;
4. Общая спецификация элементов дверных и оконных заполнений дана на листе 25 данного тома;
5. Маркировка проемов и ниш сквозная по этажу фрагмента, дана в стенах и перегородках;
6. Узлы устройства перегородок см. технологические карты, альбомы технических решений и комплектных систем производителей (см. лист 1 данного тома);
7. Уточнить раскладку балок и количество кирпичных столбиков после демонтажа напольного покрытия
8. Уточненные конструктивные схемы опирания лаг и балок представлены в томе НД-2026-1-1.1-КР
9. Реставрационные чертежи см. тома НД-2026-1-1.1-РР.АИ1-АИ3;
10. Реставрационные чертежи столярных дверных и оконных заполнений см. тома НД-2026-1-1.1-РР.ДВ, НД-2026-1-1.1-РР.ОК;
11. Рисунок штучного паркета см. л.23 данного тома.

Ведомость возводимых перегородок и стен фрагмента 5 этажа в осях 4-12/Г-С			
Марка	Наименование	Площадь, кв м	Примечание
1	Перегородка из бетонного камня	46.24	
2.2	КНАУФ перегородка типа С382	6.93	В качестве стоек каркаса использовать профиль ПС 75/50 с шагом не более 500 миллиметров
4.2	КНАУФ зашивка типа С686	25.31	В качестве стоек каркаса использовать профиль ПС 100/50 с шагом не более 500 миллиметров
5	КНАУФ перегородка типа С366	20.91	
5.2	КНАУФ перегородка на основе типа С366	310.27	
6	Кирпичная кладка	5.87	
		415.53	

Условные обозначения:

- 1 – Ось координации
- +0,000 – Отметка уровня
- Реставрируемые помещения
- Сохраняемые конструкции
- Пробиваемый проем
- Закладываемый проем
- Рядовая перегородка с обшивкой ГКЛ-листами
- Влагостойкая перегородка с обшивкой КНАУФ-листами АКВАПАНЕЛЬ
- Огнестойкая перегородка обшивкой КНАУФ-листами ФАЙЕРБОРД
- Перегородка из бетонного камня
- Д-1.1-1-1П
- 1.1 – Марка пола
- О-1.1
- См
- Сб
- Ак
- Ма
- Ма

Согласовано

Взам. инв. №

Подп. и дата

Инв. № подл.