

Маркировочный план фрагмента 5 этажа в осях 12-18/Д-Р

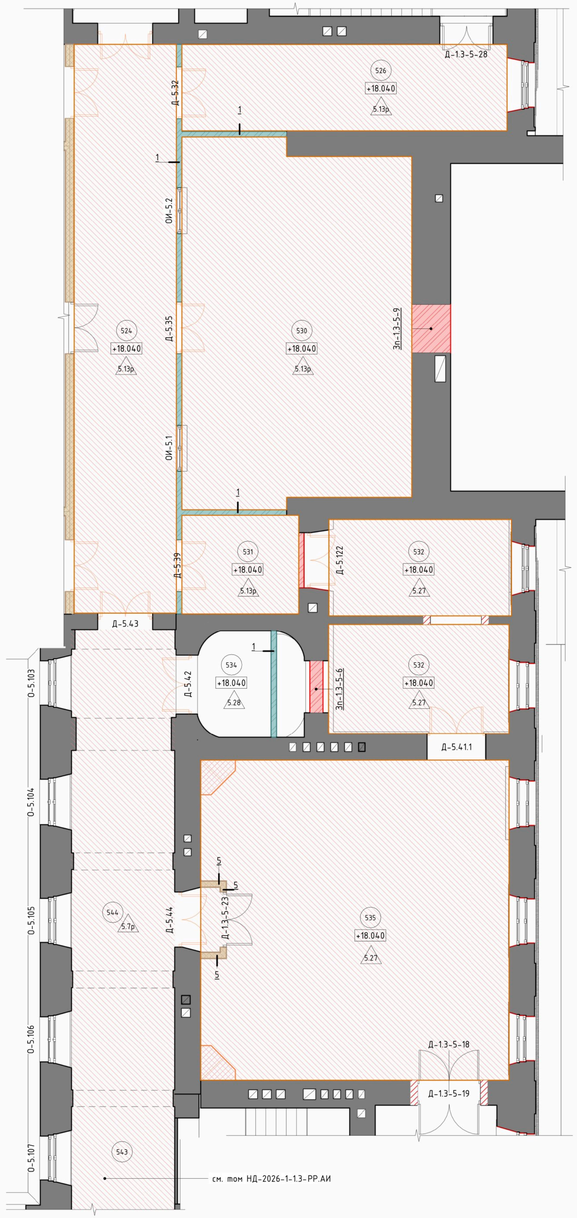

Маркировочный план фрагмента 5 этажа в осях 1-13/А-Г (1 : 75)

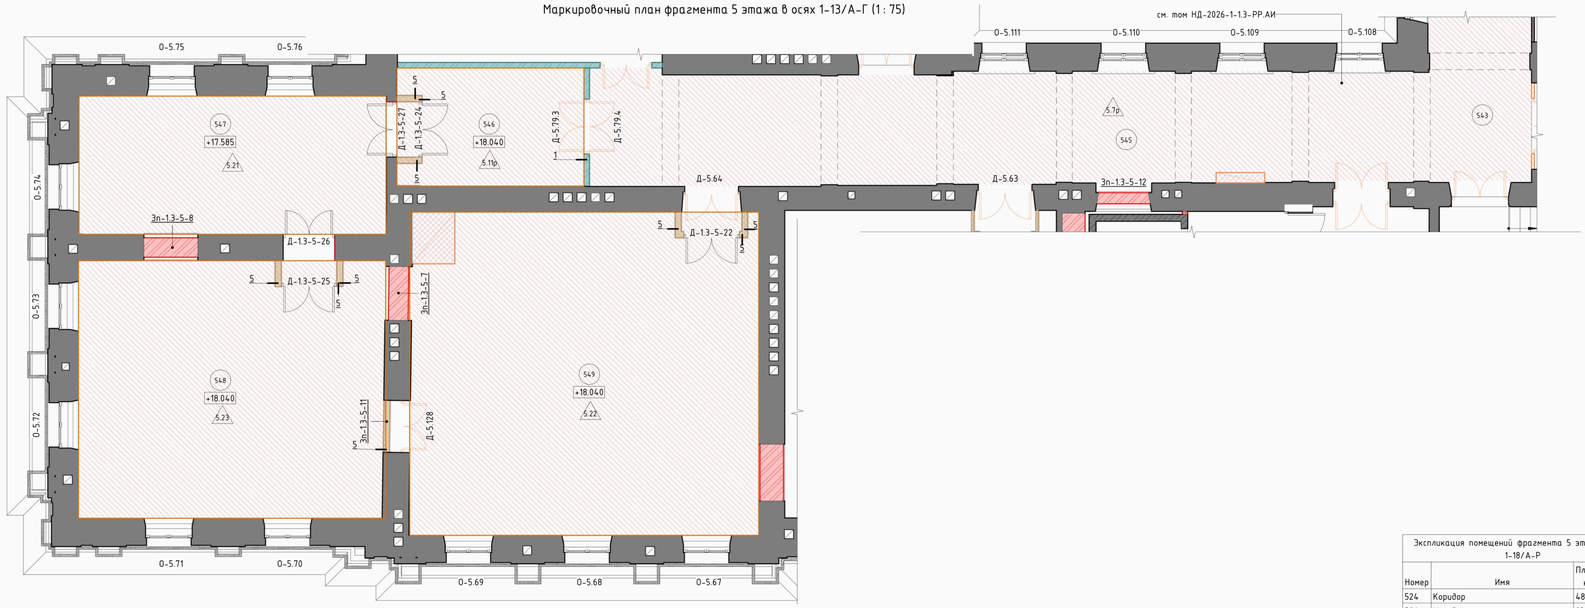

Экспликация помещений фрагмента 5 этажа в осях 1-18/А-Р

Номер	Имя	Площадь, кв. м.	Кат. пом.
524	Коридор	48.75	
526	Коридор	23.60	
530	Кладовая музыкальных инструментов	68.38	В3
531	ПУИ	9.55	В4
532	Кладовая музыкальных инструментов	31.31	В3
534	Коридор	6.26	
535	Репетиторий	82.48	
543	Коридор	55.77	
544	Коридор	29.78	
545	Коридор	54.96	
546	Коридор	18.51	
547	Репетиторий	35.55	
548	Репетиторий	65.90	
549	Репетиторий	94.33	
		625.12	

Ведомость закладываемых проемов фрагмента 5 этажа в осях 1-18/А-Р

Марка	Наименование	Объем, куб. м.	Примечание
Зп-1.3-5-5	Кирпичная кладка	0.72	
Зп-1.3-5-6	Кирпичная кладка	1.71	
Зп-1.3-5-7	Кирпичная кладка	2.56	
Зп-1.3-5-8	Кирпичная кладка	2.61	
Зп-1.3-5-9	Кирпичная кладка	3.53	
Зп-1.3-5-10	Кирпичная кладка	3.37	
Зп-1.3-5-11	КНАУФ перегородка типа С366	0.86	
Зп-1.3-5-12	Кирпичная кладка	1.37	
		16.72	

Ведомость возводимых перегородок и стен фрагмента 5 этажа в осях 1-18/А-Р

Марка	Наименование	Площадь, кв м	Примечание
1	Перегородка из бетонного камня	104.94	
5	КНАУФ перегородка типа С366	28.28	
		133.22	

Условные обозначения:

- 1 – Ось координации
- +0,000 – Отметка уровня
- Реставрируемые помещения
- Сохраняемые конструкции
- Пробиваемый проем
- Закладываемый проем
- Рядовая перегородка с обшивкой ГКЛ-листами
- Влагостойкая перегородка с обшивкой КНАУФ-листами АКВАПАНЕЛЬ
- Огнестойкая перегородка обшивкой КНАУФ-листами ФАЙЕРБОРД
- Перегородка из бетонного камня
- Смешанная перегородка
- Сборная конструкция из фанеры
- Акустическая перегородка
- Д-1.3-1-1П – Марка дверного заполнения
- О-1.1 – Марка оконного заполнения
- 1.1 – Марка пола
- Зп-1.3-1-1 – Марка закладываемого проема
- 1.1 – Марка стены
- Обмазочная гидроизоляция "мокрых" помещений

1. Данный лист смотреть совместно листами 5, 12, 15-22 данного
2. Общая спецификация возводимых стен и перегородок дана на
3. Общая спецификация экспликация устраиваемых полов дана на
4. Общая спецификация элементов дверных и оконных заполнений
5. Принципиальные решения по ремонту дверных проемов даны на
6. Маркировка проемов и ниш сквозная по этажу фрагмента, дан
7. Узлы устройства перегородок см. технологические карты, альб систем производителей (см. лист 1 данного тома);
8. Реставрационные чертежи, в том числе чертежи печей и ками
9. Реставрационные чертежи столярных дверных и оконных запол НД-2026-1-1.3-РР.ОК
10. Рисунок штучного паркета см. л 18 данного тома

Согласовано

Взам. инв. №

Подп. и дата

Инв. № подл.