
Маркировочный план фрагмента 4 этажа в осях 6-18/А-К (1 : 75)

Экспликация помещений фрагмента в осях А-К/6-18 4 этажа			
Номер	Имя	Площадь, кв. м.	Кат. пом.
406	С/У	17.62	
409	Гримерная	33.13	
410	Коридор	35.96	
411	Зона безопасности МГН	15.81	
412	Кабинет	17.96	
416	Тамбур-шлюз	5.53	
417	Коридор	6.77	
419	ПУИ	7.46	В4
420	Коридор	53.47	
Л5	Лестничная клетка (Тип ЛК: Л2)	19.87	
Л7	Технологическая лестница	23.10	
		236.68	

Ведомость возводимых перегородок и стен фрагмента в осях А-К/6-18 4 этажа			
Марка	Наименование	Площадь, кв м	Об Примечания
1	Перегородка из бетонного камня	19.97	
2.2	КНАУФ перегородка типа С382	10.84	В качестве стойек каркаса использовать профиль ПС 75/50 с шагом не более 500 миллиметров
3.1	КНАУФ перегородка типа на основе С135	18.76	
4.2	КНАУФ зашивка типа С686	56.86	В качестве стойек каркаса использовать профиль ПС 100/50 с шагом не более 500 миллиметров
		106.42	

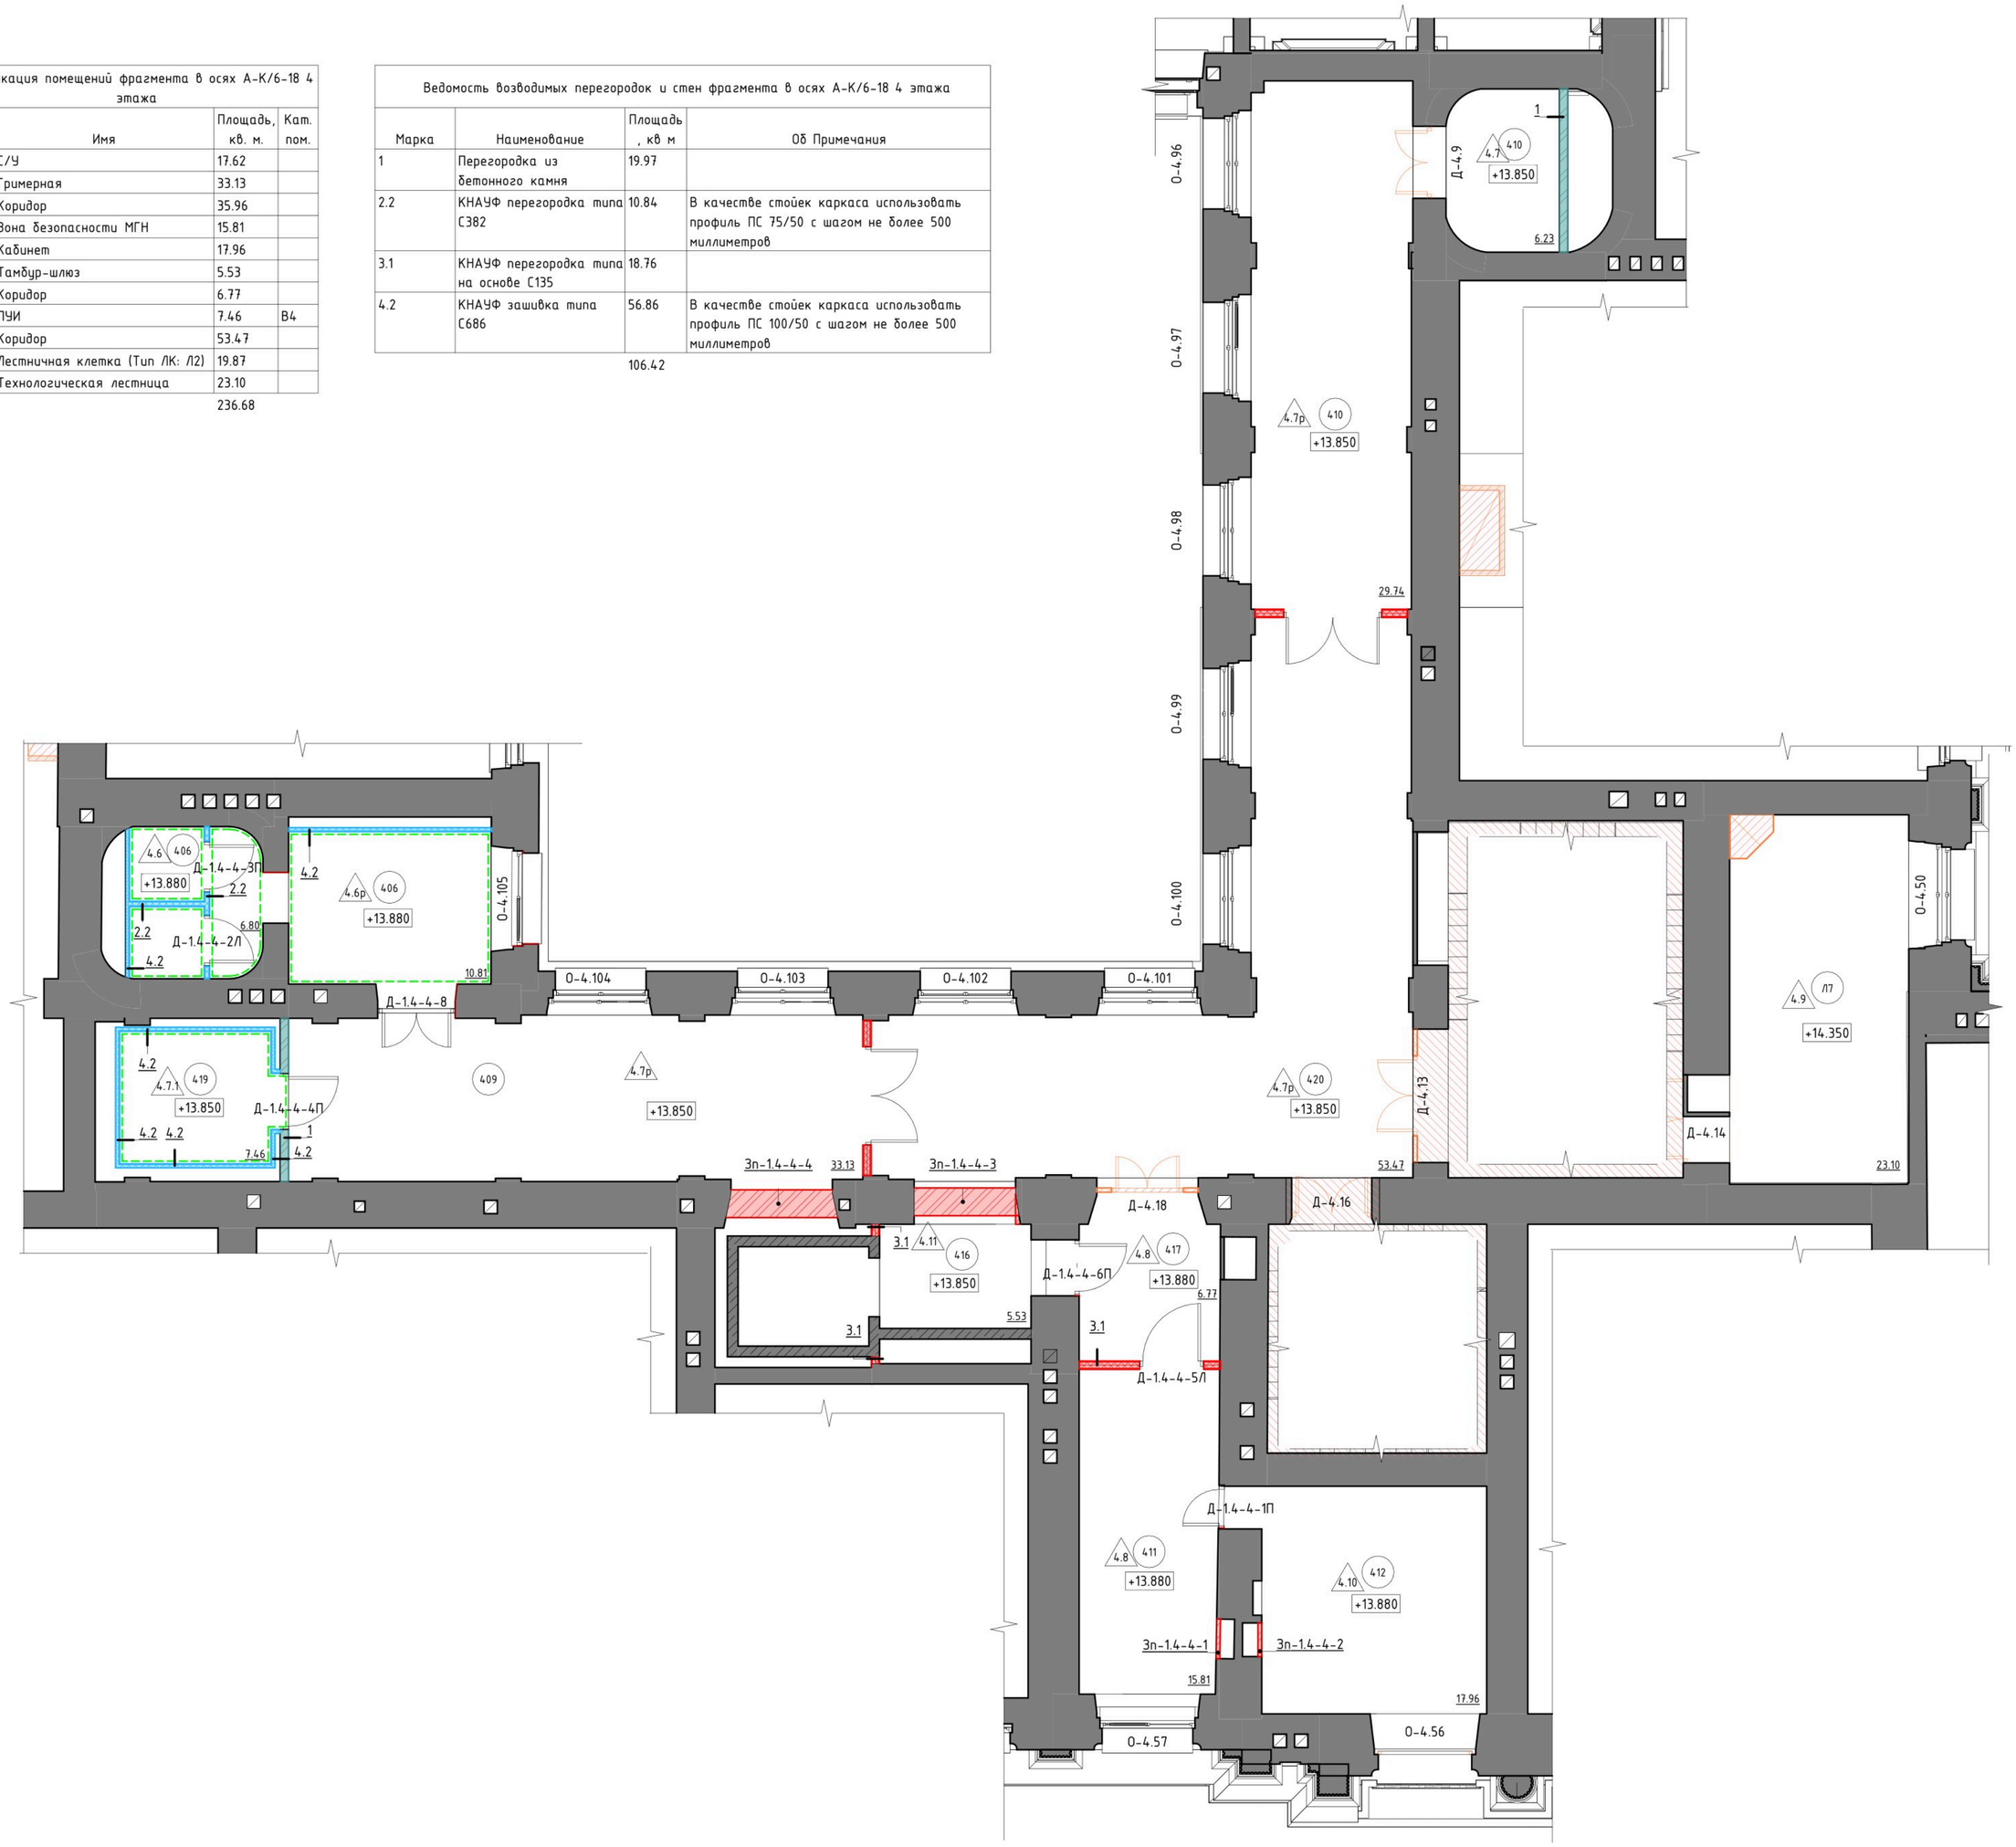

Условные обозначения:

- 1 – Ось координации
- +0,000 – Отметка уровня
- – Реставрируемые помещения
- – Сохраняемые конструкции
- – Пробиваемый проем
- – Закладываемый проем
- – Рядовая перегородка с обшивкой ГКЛ-листами
- – Влагостойкая перегородка с обшивкой КНАУФ-листами АКВАПАНЕЛЬ
- – Огнестойкая перегородка обшивкой КНАУФ-листами ФАЙЕРБОРД
- – Перегородка из бетонного камня
- 1.1 – Марка пола
- – Смешанная перегородка
- – Сборная конструкция из фанеры
- – Акустическая перегородка
- Д-1.1-1-1П – Марка дверного заполнения
- О-1.1 – Марка оконного заполнения
- Зп-1.1-1-1 – Марка закладываемого проема
- 1.1 – Марка стены
- – Обмазочная гидроизоляция "мокрых" помещений
- – Закладываемый проем

1. Данный лист смотреть совместно листами 6, 12.1, 20-24 данного тома;
2. Общая спецификация возводимых стен и перегородок дана на листе 22 данного тома
3. Общая спецификация экспликация устраиваемых полов дана на листах 20-21 данного
4. Общая спецификация элементов дверных заполнений дана на листах 23-24 данного т
5. Маркировка проемов и ниш сквозная по этажу фрагмента, дана в стенах и перегород
6. Узлы устройства перегородок см. технологические карты, альбомы технических реше производителей (см. лист 1 данного тома);
7. Уточнить раскладку балок и количество кирпичных столбиков после демонтажа напо
8. Уточненные конструктивные схемы опирания лаг и балок представлены в томе НД-20
9. Реставрационные чертежи см. тома НД-2026-1-1.1-РР.АИ1-АИ3;
10. Реставрационные чертежи столярных дверных и оконных заполнений см. тома НД-202
11. Рисунок штучного паркета см. л.21 данного тома.

Согласовано

Взам. инв. №

Подп. и дата

Инв. № подл.

Номер помещен
4
406
406
409, 410, 420
419
409, 410, 420
411, 417
403
412
416