Маркировочный план фрагмента в осях 9-20/А-Д 5 этажа (1: 75)

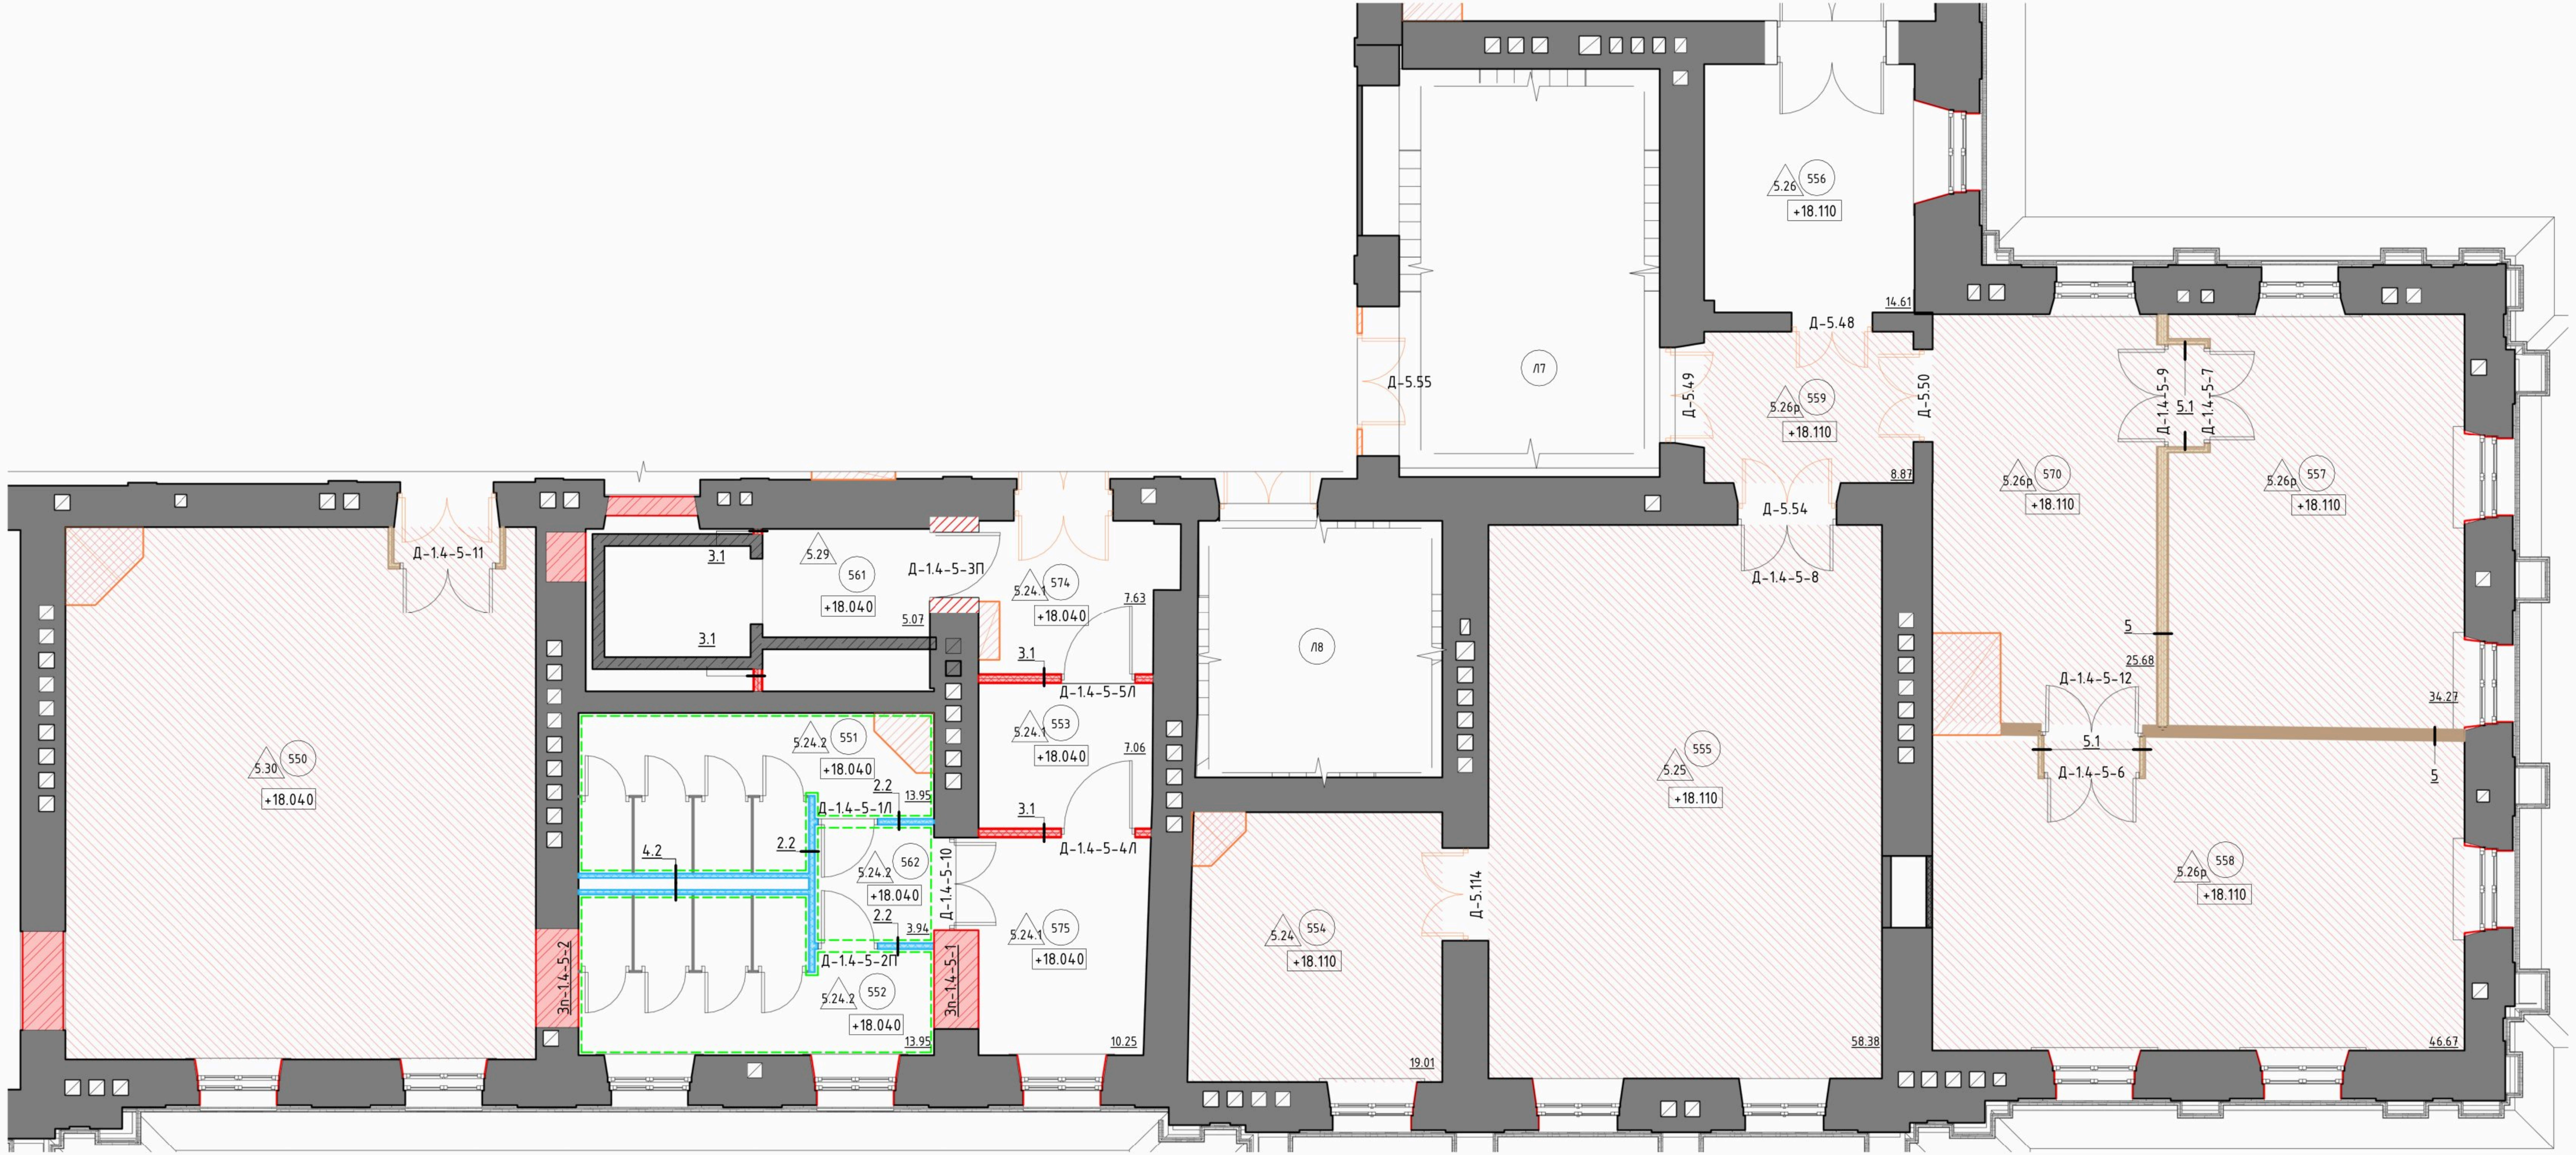

Экспликация помещений фрагмента в осях 7-20/А-Д 5 этажа

Номер	Имя	Площадь, кв. м.	Кат. пом.
550	Репетиторий	70.04	
551	С/У М	13.95	
552	С/У Ж	13.95	
553	Зона безопасности МГН	7.06	
554	Кладовая музыкальных инструментов	19.01	В3
555	Репетиторий	58.38	
556	Комната настройки музыкальных инструментов	14.61	
557	Репетиторий	34.27	
558	Репетиторий	46.67	
559	Комната ожидания артистов	8.87	
561	Тамбур-шлюз	5.07	
562	Коридор	3.94	
570	Гримерная	25.68	
574	Коридор	7.63	
575	Коридор	10.25	
		339.39	

Ведомость возводимых перегородок и стен фрагмента в осях 9-20/А-Д 5 этажа

Марка	Наименование	Площадь, кв м	Примечание
2.2	КНАУФ перегородка типа С382	18.25	
3.1	КНАУФ перегородка типа на основе С135	22.95	
4.2	КНАУФ зашивка типа С686	23.83	
5	КНАУФ перегородка типа С366	24.74	
5.1	Перегородка звукоизоляционная 90 мм	18.80	
		108.57	