
Дворец. План 1 этажа (1:200)

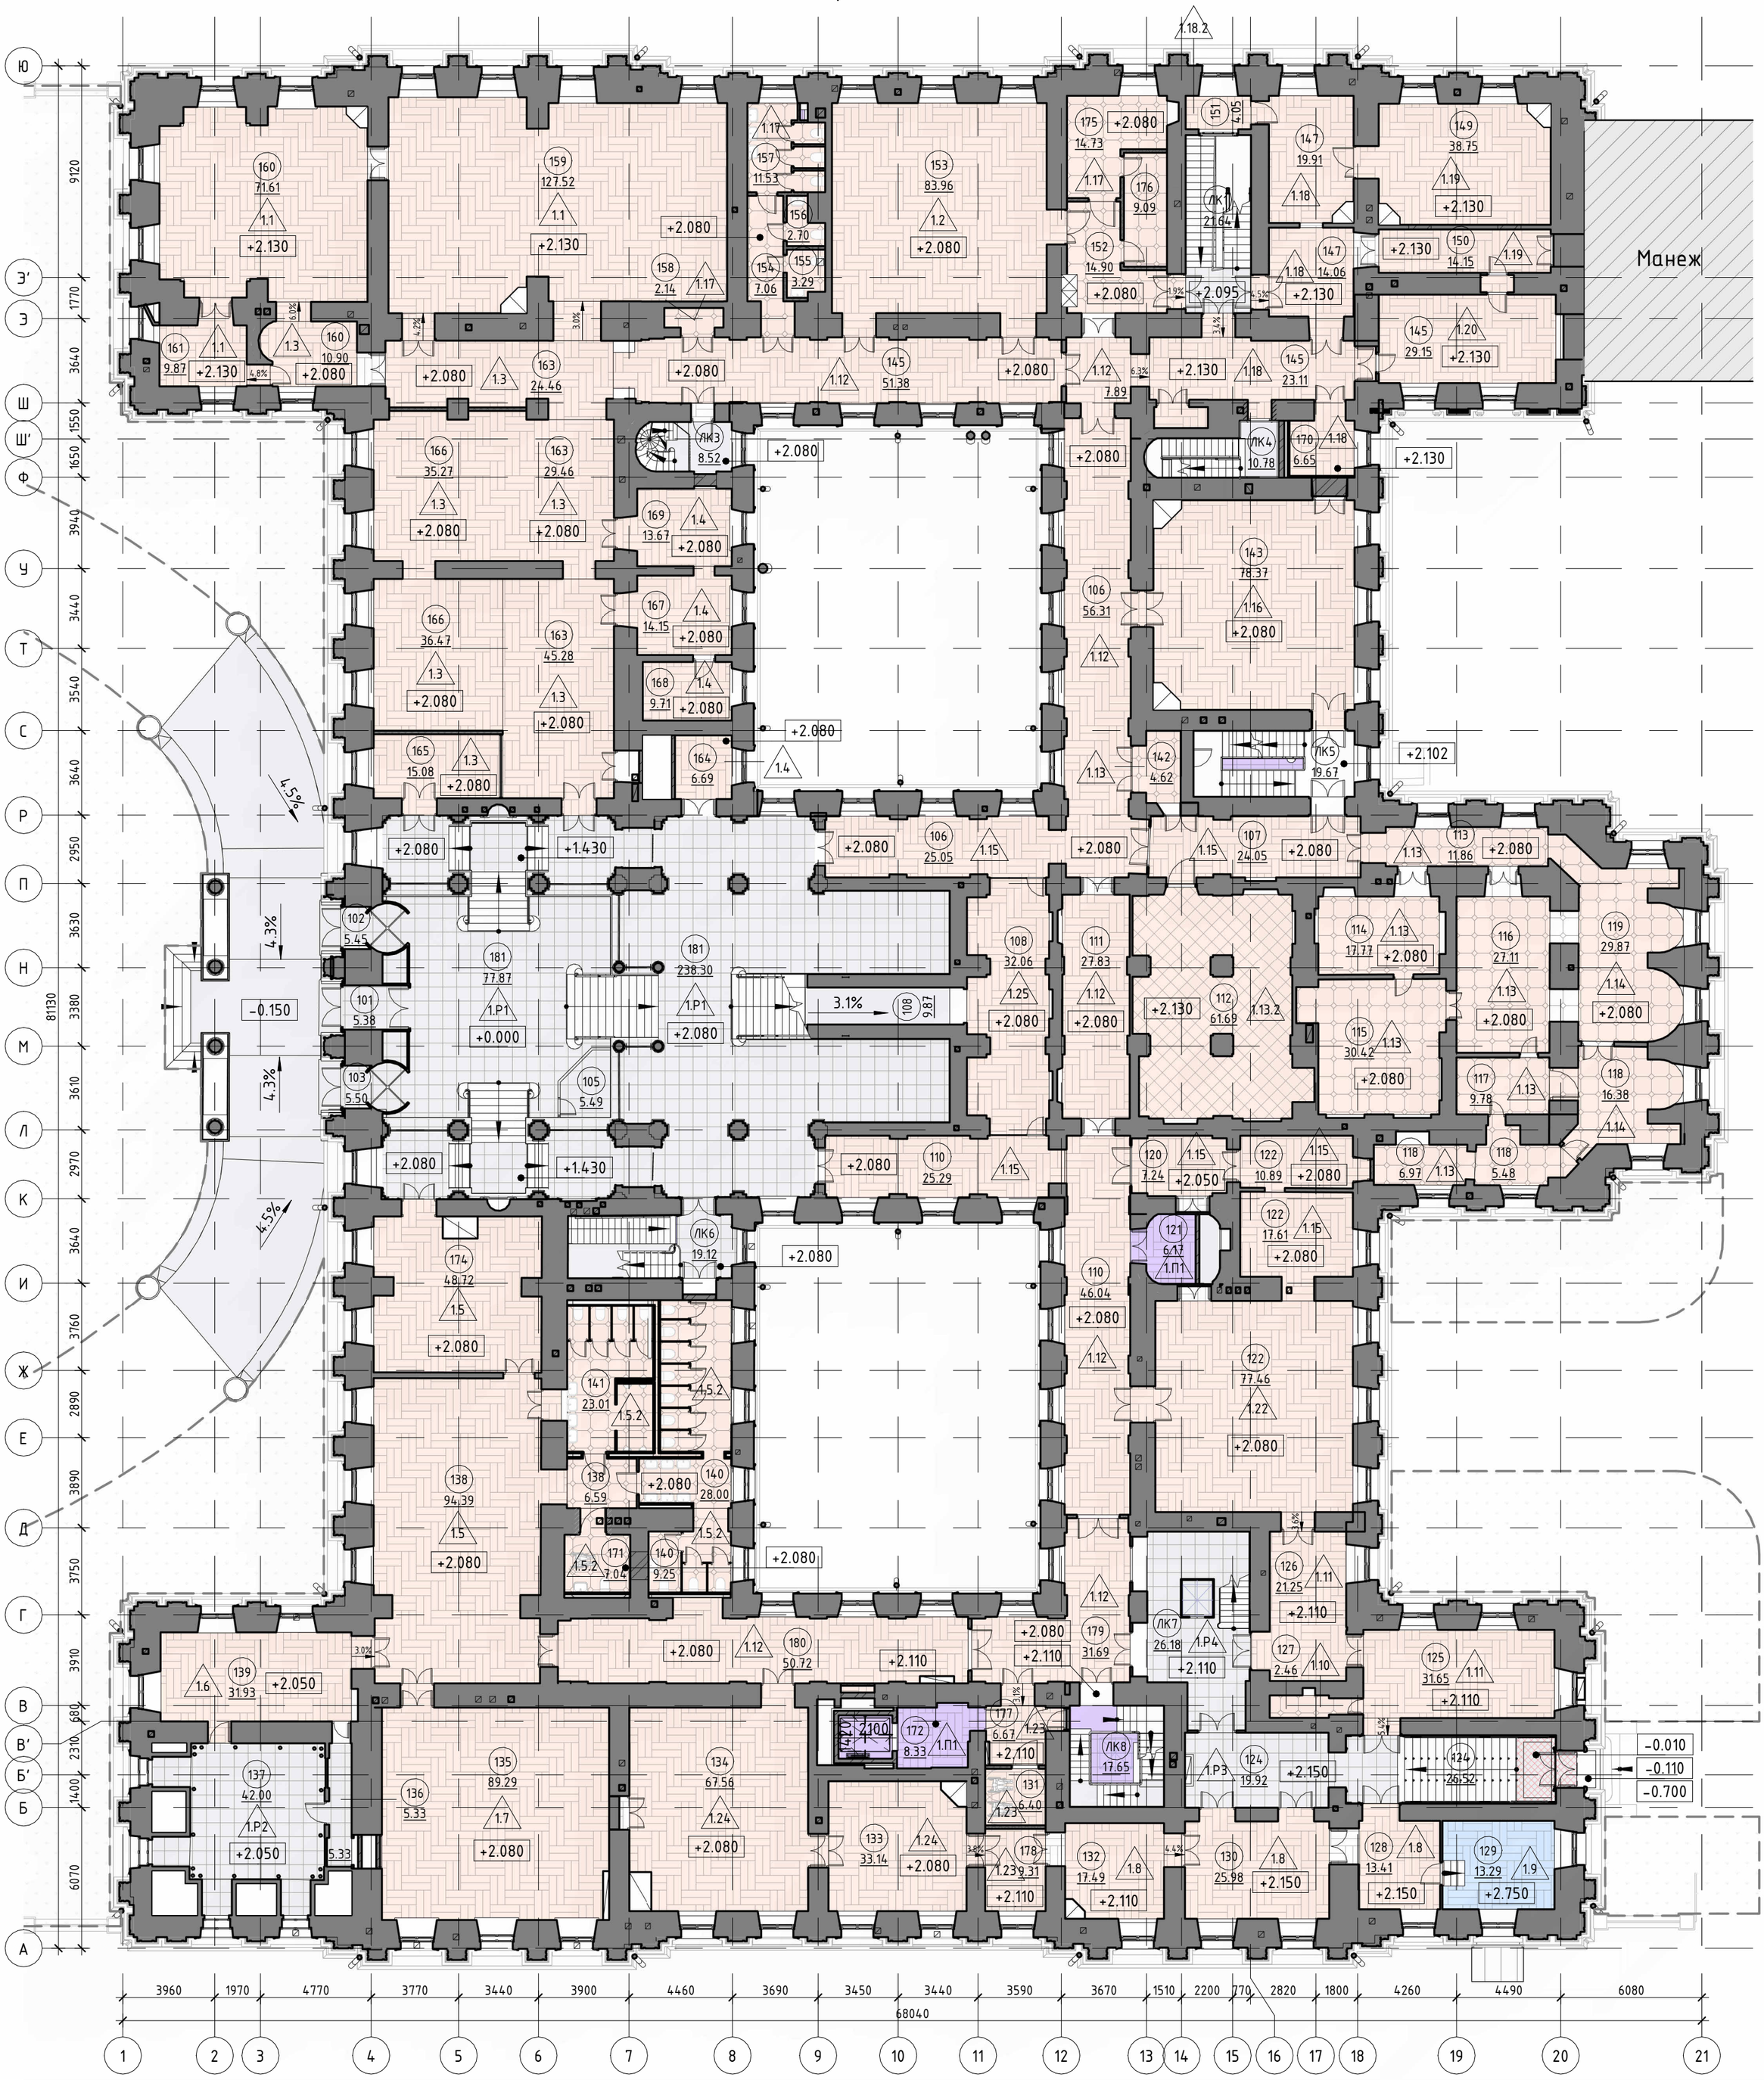

1. Предусмотреть стыковку пола со стенами, перегородками, колоннами и другими выступающими конструкциями через демпферную ленту. При устройстве пола завести деформационный шов на 30 мм выше отметки чистого пола. После монтажа чистого пола выполнить герметизацию шва нетвердеющим герметикам.
2. Для «плавающих» полов по периметру помещений выполнить стыковку пола со стенами, перегородками, колоннами и другими выступающими конструкциями через акустический шов с заполнением – Пенополиэтилен сшитый Пенолон 3010 или ИЗОЛОН – 10 мм. Завести акустический шов на 30 мм выше отметки чистого пола. После монтажа чистого пола выполнить герметизацию шва нетвердеющим герметикам типа ВИБРОСИЛ
3. В мокрых помещениях завести обмазочную гидроизоляцию на стену на высоту 200 мм. Для бетонный оснований и кирпичных стен в подвале – гидроизоляция на цементной основе в комбинации с латексной мастикой в 2 слоя по технологии производителя. Для кирпичных стен выше подвала – выполнить выравнивание стен простой штукатуркой, грунтовку,
обмазку гидроизоляцией КНАУФ-Флэхендихт в 2 слоя по технологии производителя. Для гипсокартонных и гипсоволокнистых листов – выполнить обмазку гидроизоляцией КНАУФ-Флэхендихт в 2 слоя по технологии производителя.
4. Толщина слоя керазита показана условно. Керамзит в полу укладывается в пазухи сводов, между лаг и балок до уровня верха лаг, после укладки пролить цементным молочком.
5. Фанерные листы укладываются в 2 слоя щитами в шахматном порядке, со швами между слоями «в разбежку». Между собой листы крепятся на клей и саморезы.
6. Деревянные элементы полов выполнить из древесины, обработанной антипереном и антисептиком. Существующие элементы также необходимо обработать антипереном и антисептиком.
7. Все применяемые в отделке помещений материалы должны иметь пожарные и гигиенические сертификаты для внутренних работ в помещениях.

Условные обозначения:

- Перекрытия по сводам
- Перекрытия по металлическим балкам
- Перекрытия по деревянным балкам
- Проектируемые Ж/Б перекрытия
- Реставрируемые полы
- Паркет
- Керамогранит
- Камень
- Плавающий пол

Изм.	Кол.уч.	Лист	№док.	Подпись	Дата
Разработал		Бушуев			06.26
Разработал		Крысанова			06.26
Рук. проекта		Суша			06.26
ГИП		Чапова			06.26
ГАП		Новикова			06.26
Н. контр.		Шапченко			06.26

г. Санкт-Петербург, пл. Труда, д. 4, литера В

«Ремонт, реставрация и приспособление для современного использования (капитальный ремонт, оснащение технологическим оборудованием, в том числе проектирование) объектов культурного наследия федерального значения «Дворец», «Манеж», «Корпус служебный», «Конюшни главные дворцовые», «Конюшни дежурные», расположенных по адресу: г. Санкт-Петербург, пл. Труда, д. 4, литера В, входящих в состав объекта культурного наследия федерального значения «Дворец Великого князя Николая Николаевича (Ксенинский институт)»

Стадия	Лист	Листов
	03	

«Дворец». План полов 1 этажа

ОБЩЕСТВО С ОГРАНИЧЕННОЙ ОТВЕТСТВЕННОСТЬЮ **НИиПИ СПЕЦРЕСТАВРАЦИЯ**

Согласовано

Взам. инв. №

Подп. и дата

Инв. № подл.

A2 (420x594)