

Дворец. План 3 этажа (1:200)

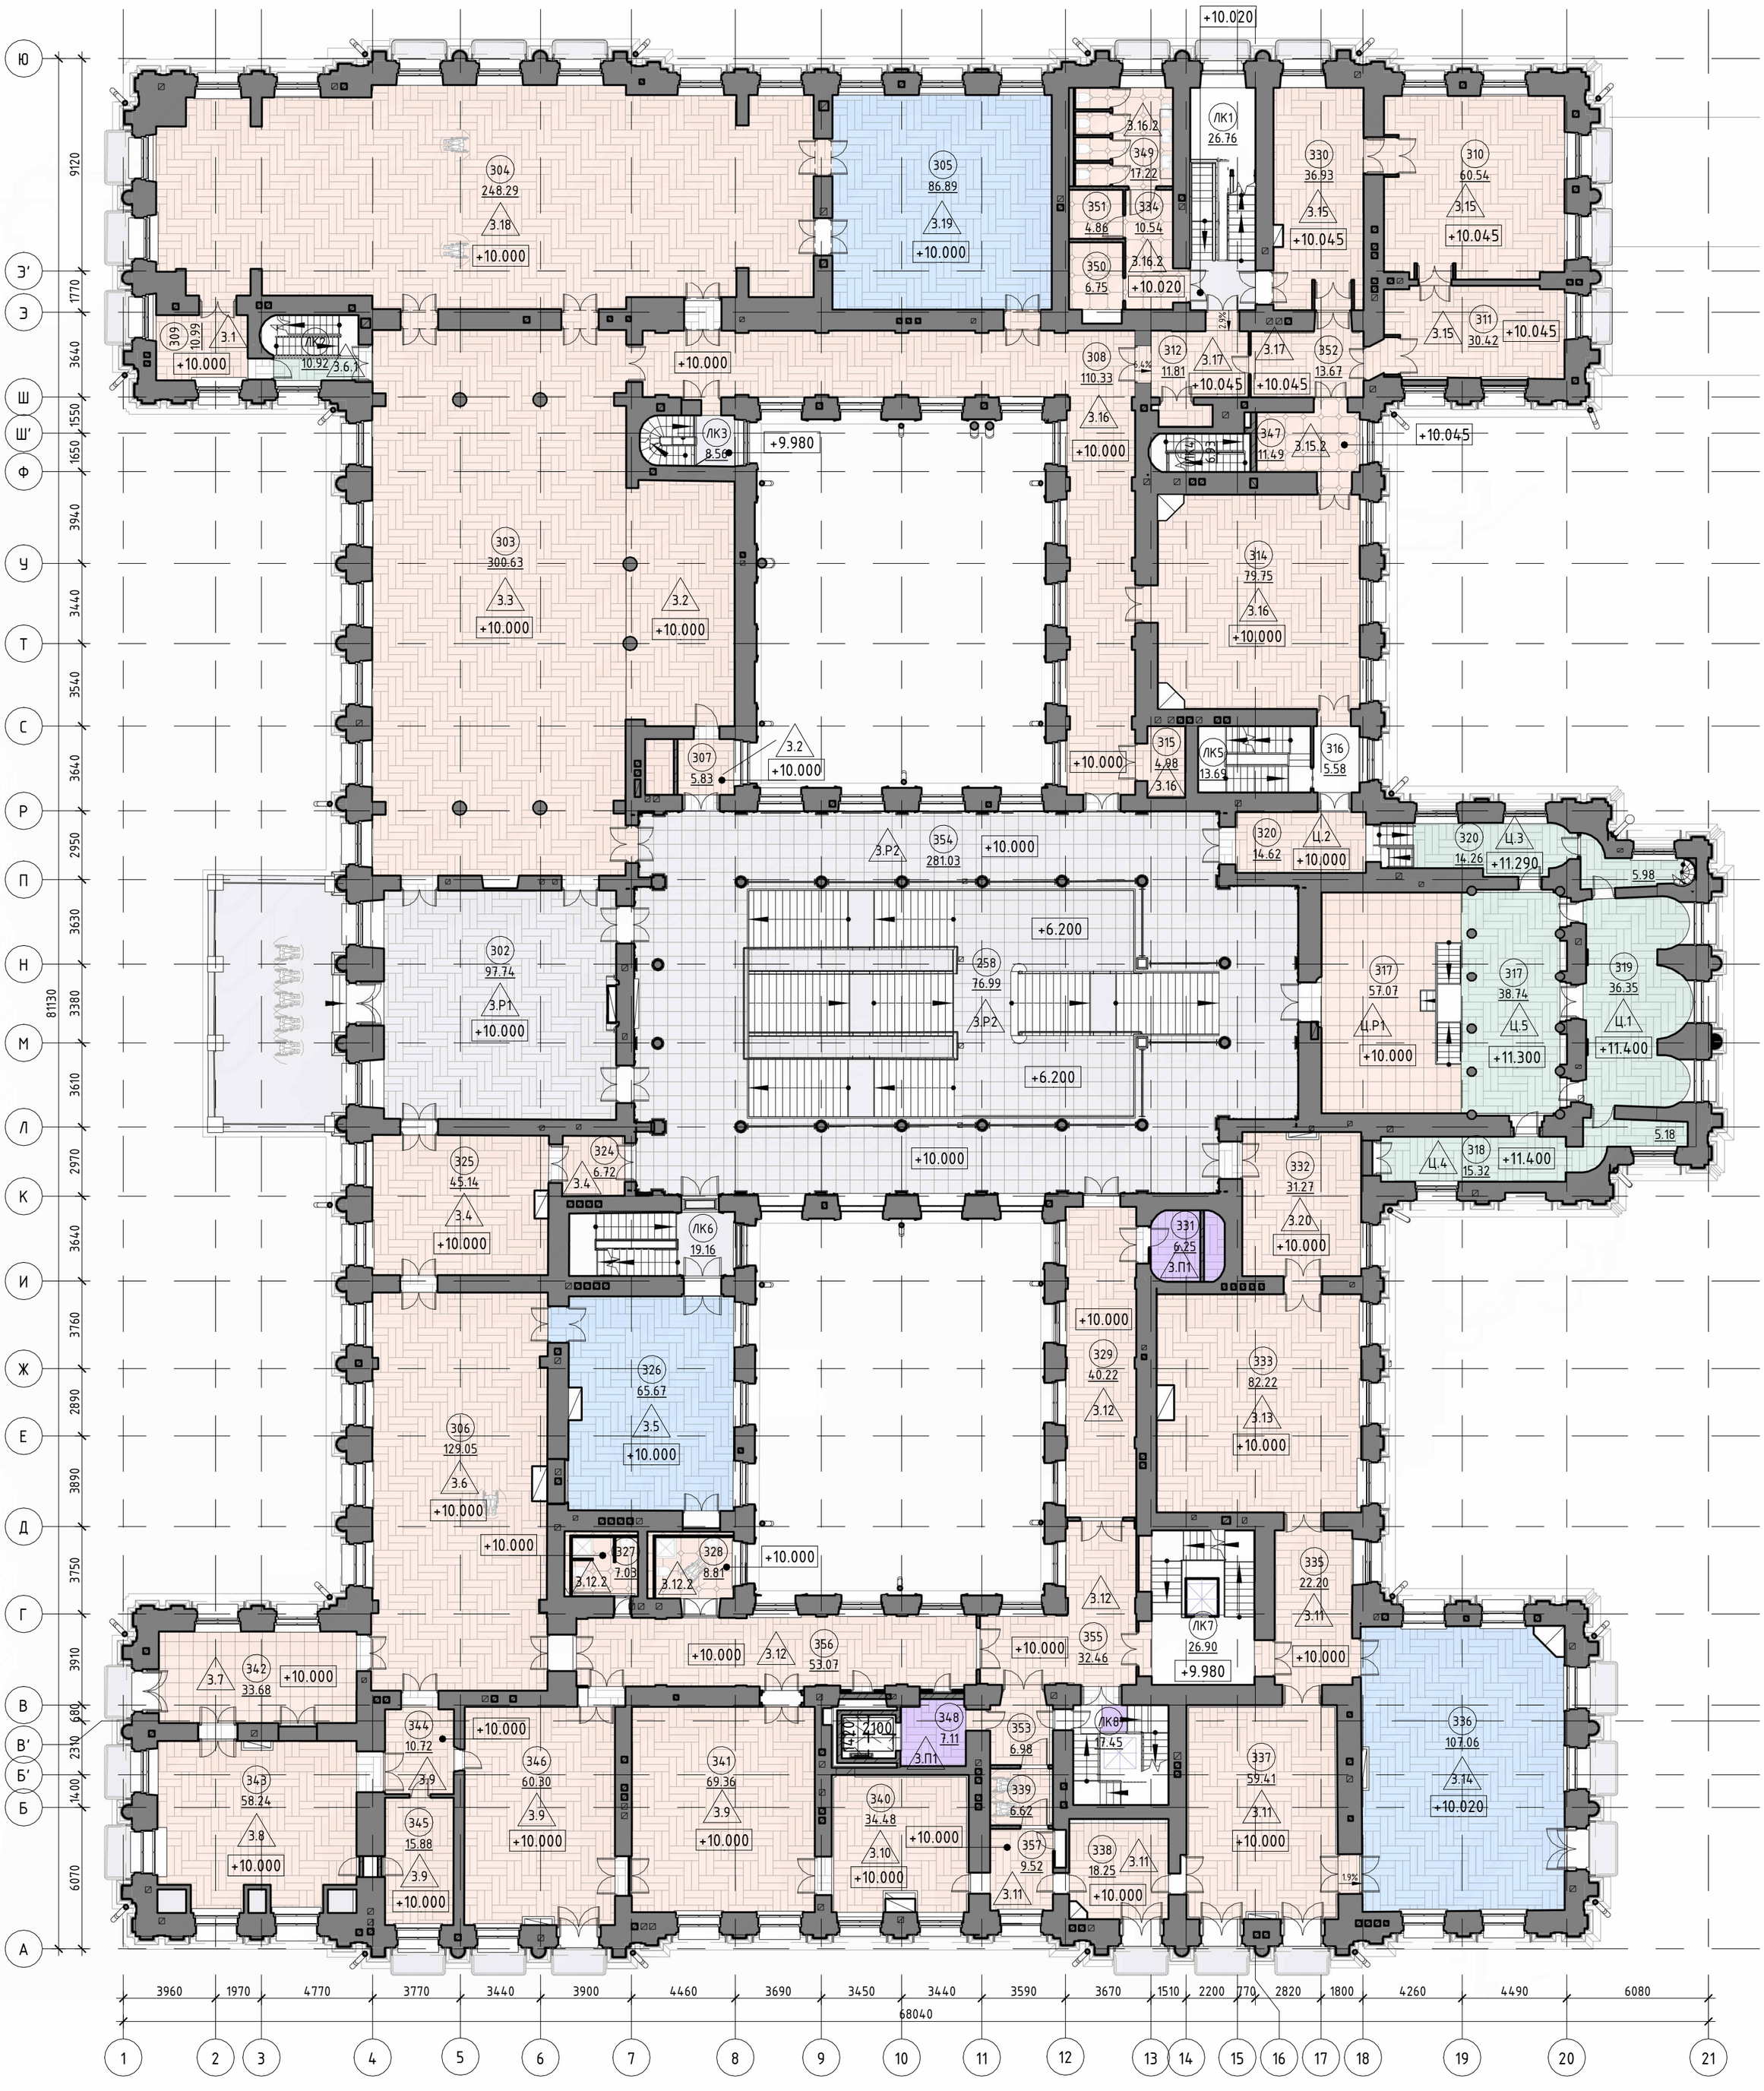

Дворец. План на отм. +10.000 этажа (1:200)

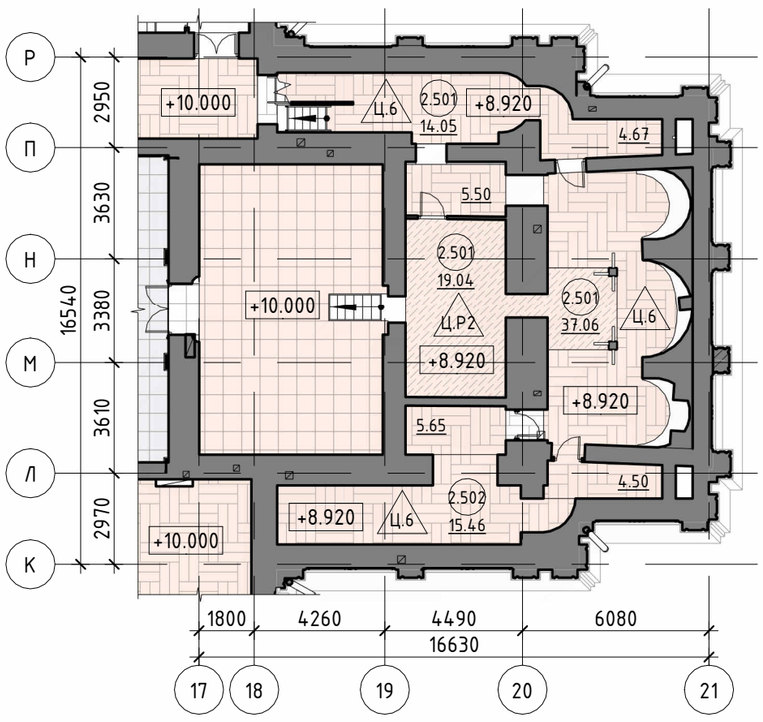

Условные обозначения:

- Перекрытия по сводам
- Перекрытия по металлическим балкам
- Перекрытия по деревянным балкам
- Проектируемые Ж/Б перекрытия
- Реставрируемые полы
- Паркет
- Керамогранит
- Камень
- Плавающий пол

Изм.	Кол.уч.	Лист	№док.	Подпись	Дата
Разработал		Бушуев			06.26
Разработал		Крысанова			06.26
Рук. проекта		Суша			06.26
ГИП		Чапова			06.26
ГАП		Новикова			06.26
Н. контр.		Шапченко			06.26

г. Санкт-Петербург, пл. Труда, д. 4, литера В

«Ремонт, реставрация и приспособление для современного использования (капитальный ремонт, оснащение технологическим оборудованием, в том числе проектирование объектов культурного наследия федерального значения «Дворец», «Манеж», «Корпус служебный», «Конюшни главные дворцовые», «Конюшни дежурные», расположенных по адресу: г. Санкт-Петербург, пл. Труда, д. 4, литера В, входящих в состав объекта культурного наследия федерального значения «Дворец Великого князя Николая Николаевича (Ксенинский институт)»

Стадия	Лист	Листов
	07	

«Дворец». План полов 3 этажа

ОБЩЕСТВО С ОГРАНИЧЕННОЙ ОТВЕТСТВЕННОСТЬЮ
НИиПИ СПЕЦРЕСТАВРАЦИЯ

Согласовано

Взам. инв. №

Подл. и дата

Инв. № подл.

А2 (420x594)